


PROPERTY AND CONFIDENTIAL THE INFORMATION CONTAINED IN THIS DRAWING THE SOLE PROPERTY OF KSQUARE ENERGY ANY REPRODUCTION IN PART OR AS A WHOLE, THE WITHOUT THE WRITTEN PERMISSION OF KSQUARE ENERGY IS PROHIBITED.

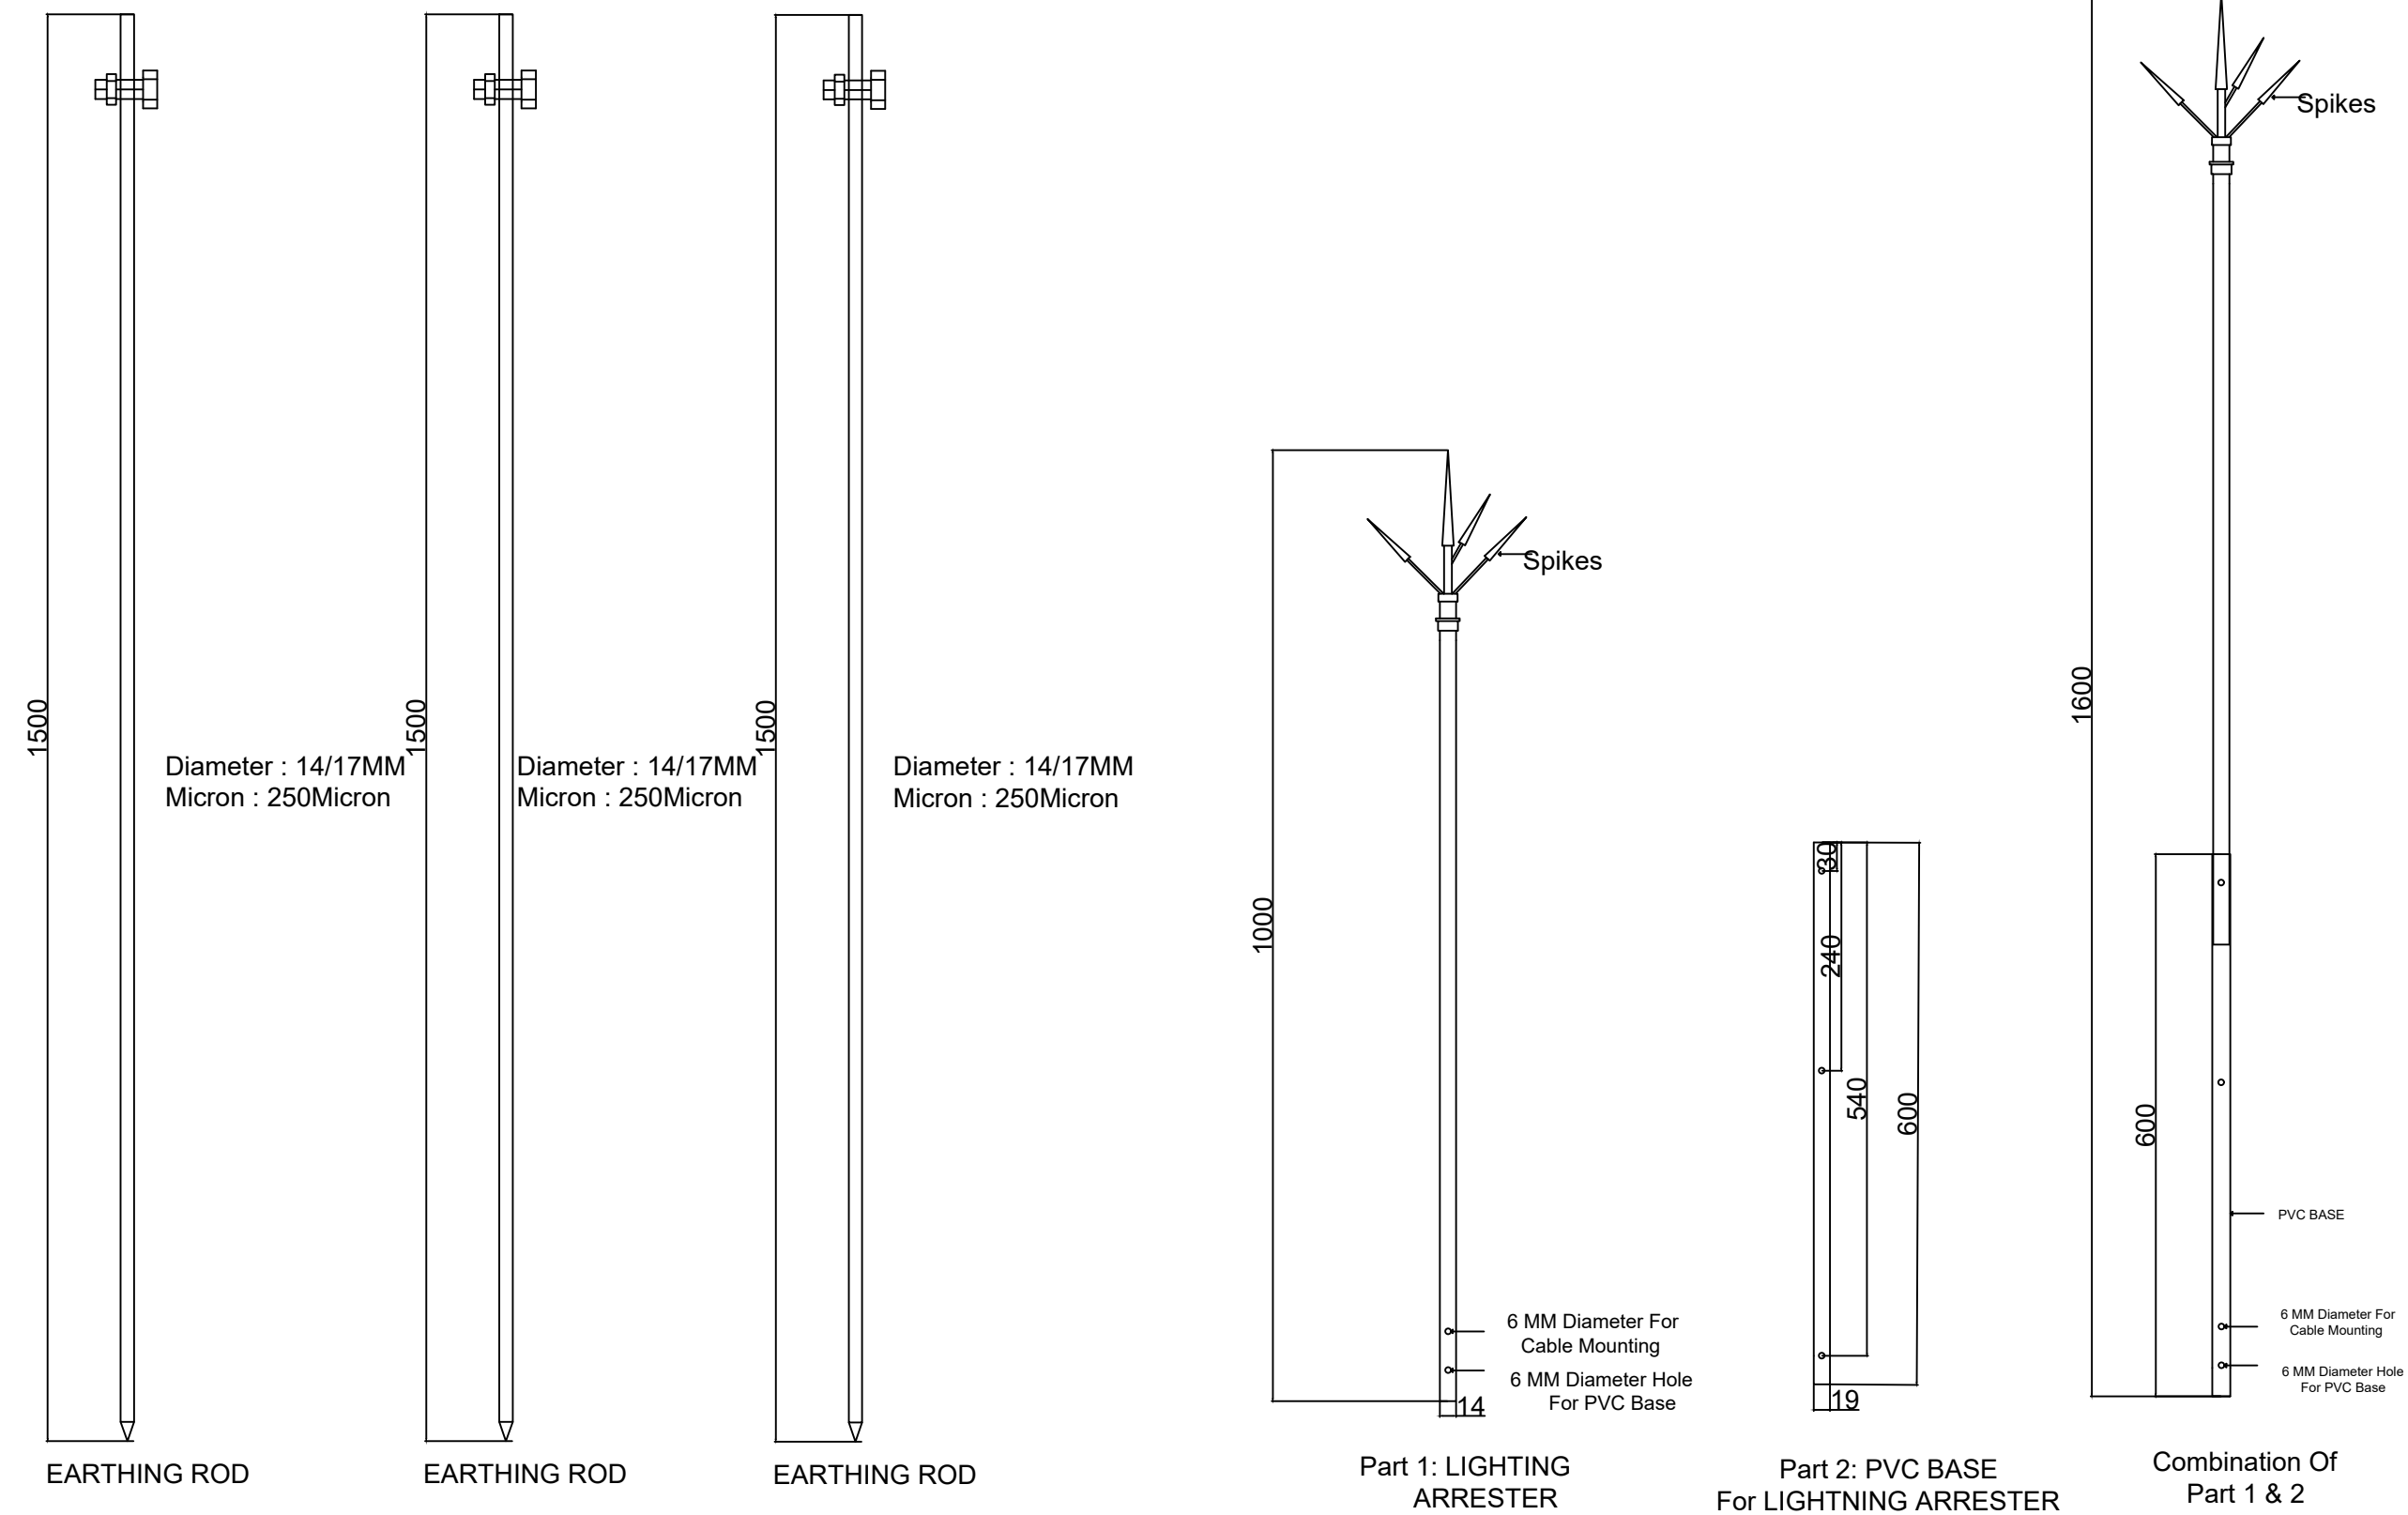

- The Solar Earthing Kit Includes
1. Earthing Rod Diameter 14/17 MM
 2. LA Rod Of 14MM Diameter & LA Spikes
 3. LA PVC Base.
 4. Mounting Kit (5 Bolt , 5 Nut ,2 Jasadi Khilla)

					KSQUARE ENERGY A - 301 , SIGNATURE 2 , SAEKHEJ SANAND CROSS ROAD, SARKHEJ, OFF. SG HIGHWAY AHMEDABAD, GUJARAT. ALL DIMENSIONS ARE IN MM TOLLERANCE ON FAB ITEM: (UNLESS OTHERWISE SPECIFIED) OVERALL DIMENSIONS: ± MM HOLE CENTERS: ± 1.0MM HOLE DIAMETER: ± 0.5MM					
01	29/11/2019									
REV	DATE :	DESCRIPTION	CHD	APD	TITLE :	PGVCL Earthing Kit	DESIGNED		CHECKED	KS
CLIENT :					DRAWING NO :	01	DRAWN	MD	APPROVED	
PROJECT :		Earthing Kit Drawing			RELEASED FOR	☒ APPROVEMENT	PROJECTION : 		SHEET : 01	REV -01